



Lámina de plantillas (lib/sheets)

1. Planta de ubicación

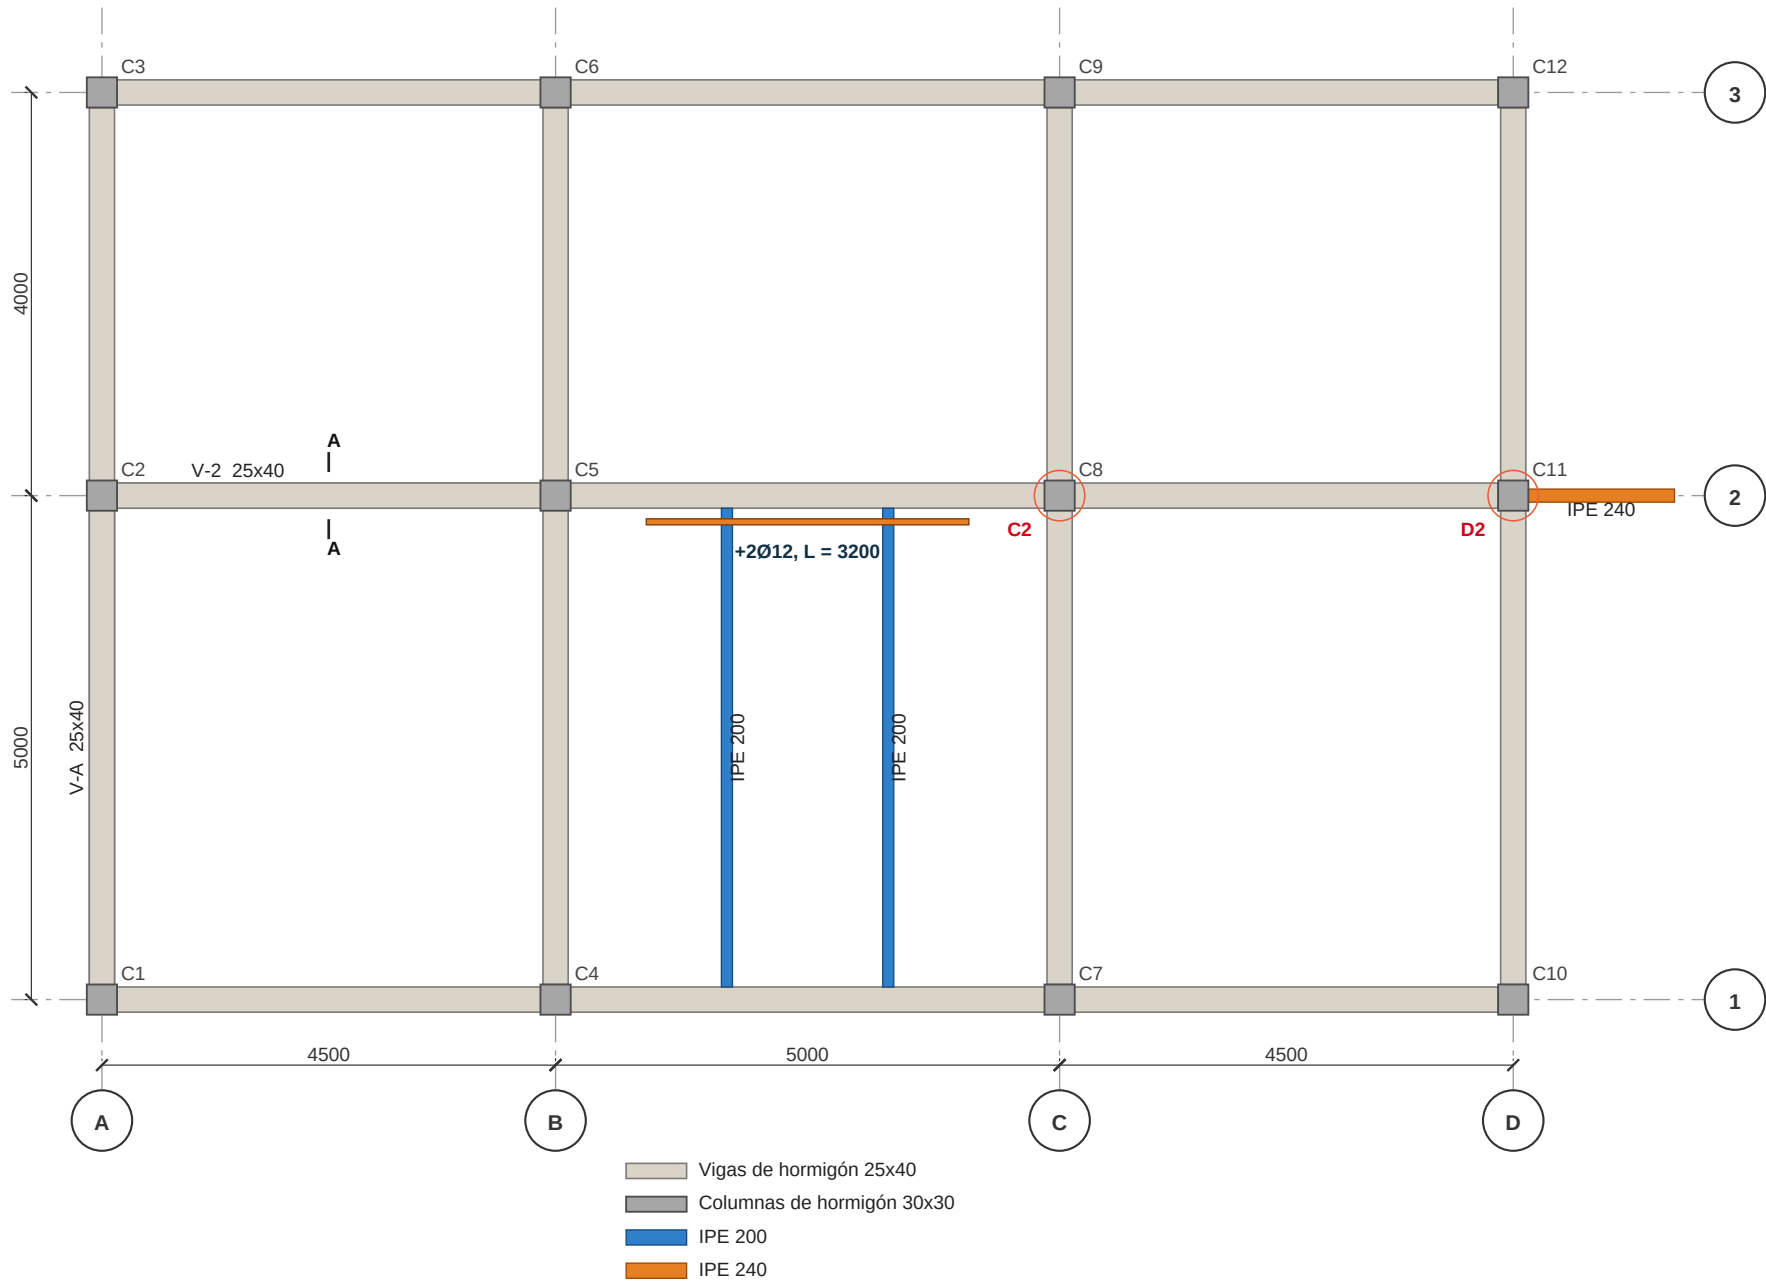


PLANTA DE UBICACIÓN ESC 1:75
c_grid, c_member, c_column_mark, c_node, c_rebar, c_cutmark, c_dim_chain, c_legend

3. Conexión placa extremo (D2)

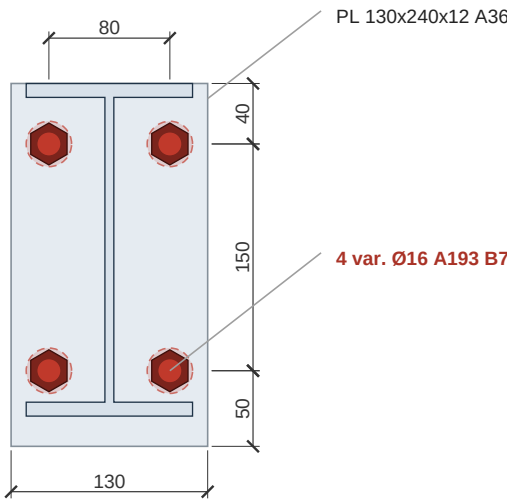


VISTA DE FRENTE ESC 1:5
c_plate + c_ishape + c_nut_front + c_leader

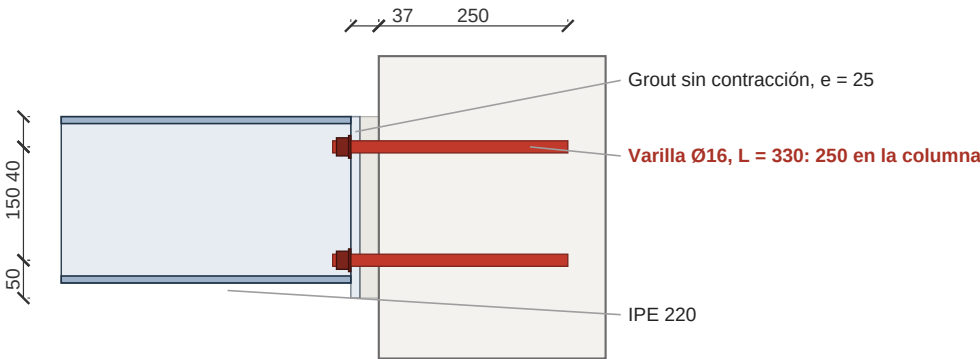


ELEVACIÓN ESC 1:10
c_ishape (elevación) + c_nut + c_leader

2. Secciones de hormigón

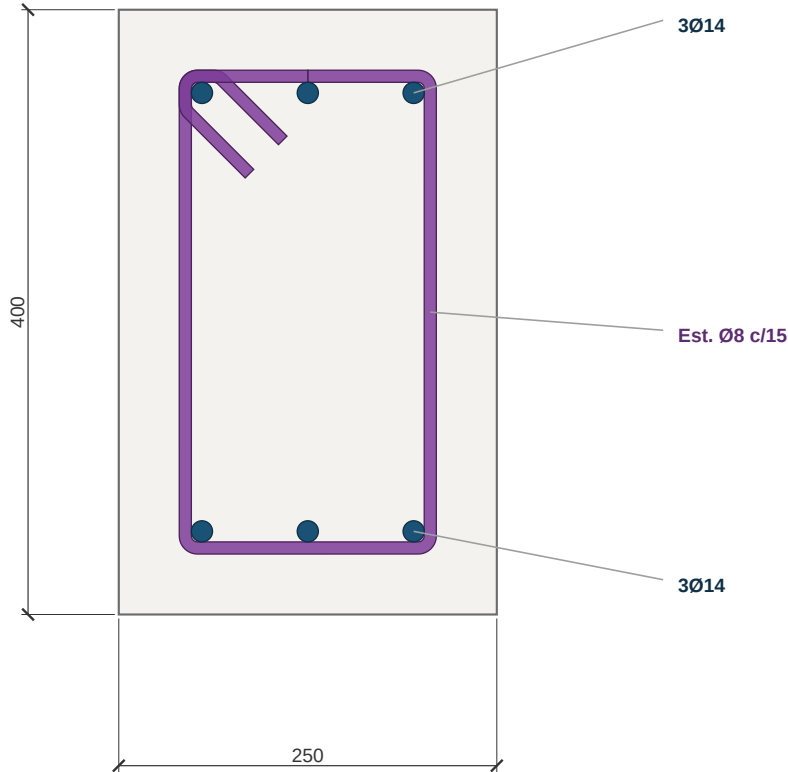


CORTE A-A: V-2 25x40 ESC 1:5
c_rc_section + c_rc_dims + c_rc_labels

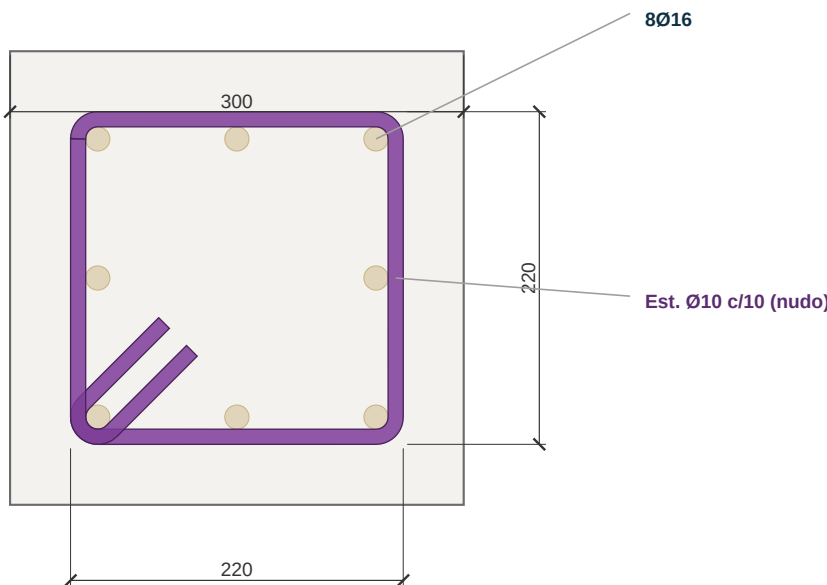


COLUMNA C 30x30 ESC 1:5
c_column_tie (cota interior: estribo) + c_rc_labels


4. Piezas, cantidades y notas

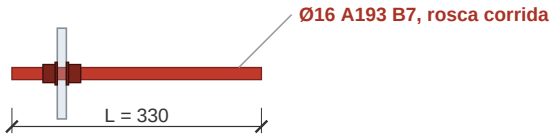

A1: VARILLA ESC 1:10
c_nut a cada lado de una placa

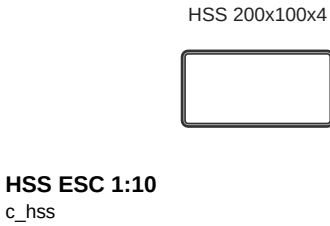

HSS ESC 1:10
c_hss

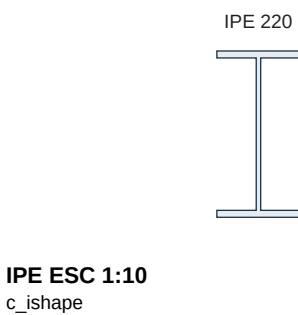

IPE ESC 1:10
c_ishape

Cantidades (blk_table)

Marca	Elemento	Descripción	Cant.
A1	Varilla	Ø16 A193 B7, L = 330	4
P2	Placa extremo	PL 130x240x12 A36, 4 agujeros Ø18	1
T	Tuerca	Ø16 grado 8	4
BA	Barra extra	2Ø12, L = 3200	2

Notas (blk_note)

- Medidas en mm.
- Hormigón f_c 21 MPa; acero de refuerzo f_y 412 MPa.
- Supuestos: longitud de varilla y tuercas grado 8 no dados en el pedido.