


Lámina de plantillas (lib/sheets)


1. Planta de ubicación

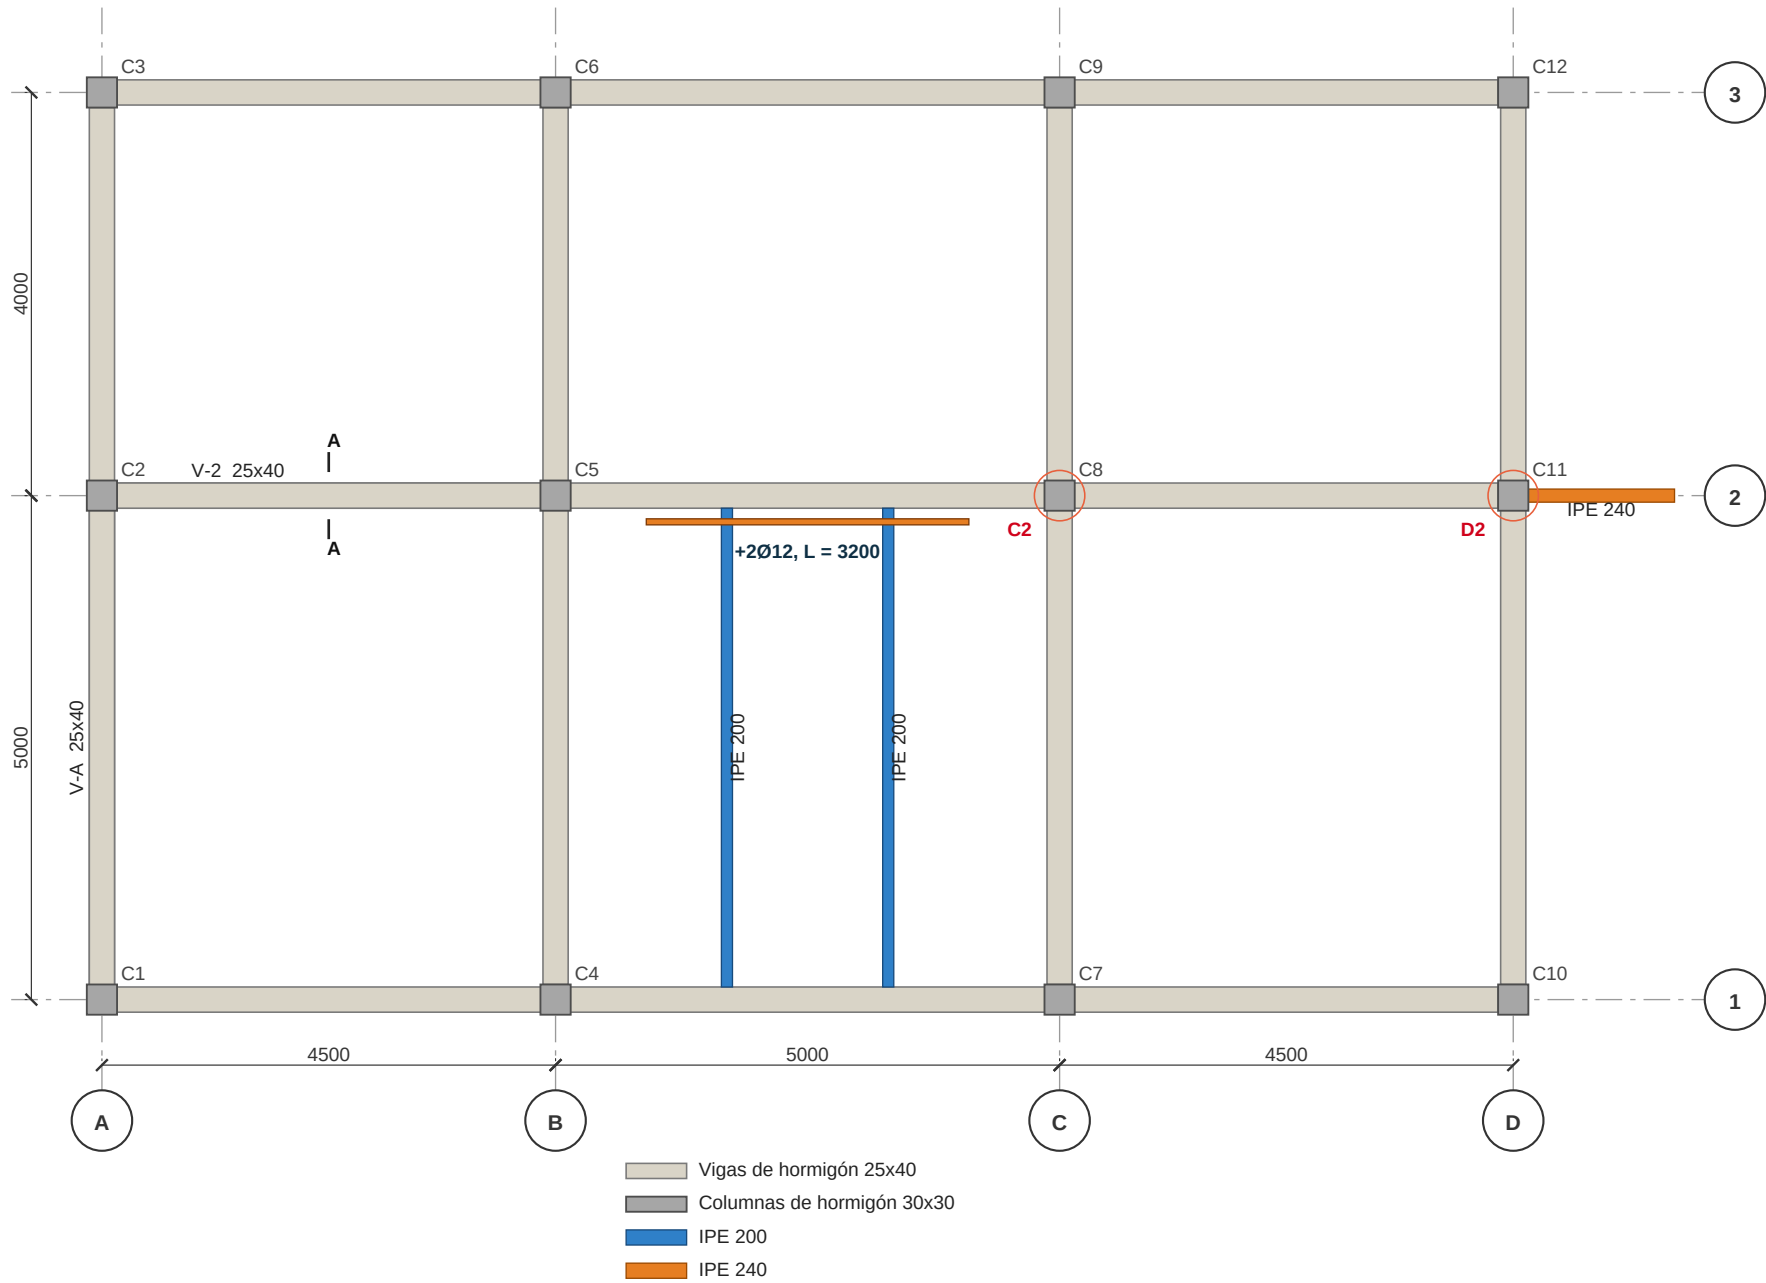

PLANTA DE UBICACIÓN ESC 1:75

c_grid, c_member, c_column_mark, c_node, c_rebar, c_cutmark, c_dim_chain, c_legend


3. Conexión placa extremo (D2)

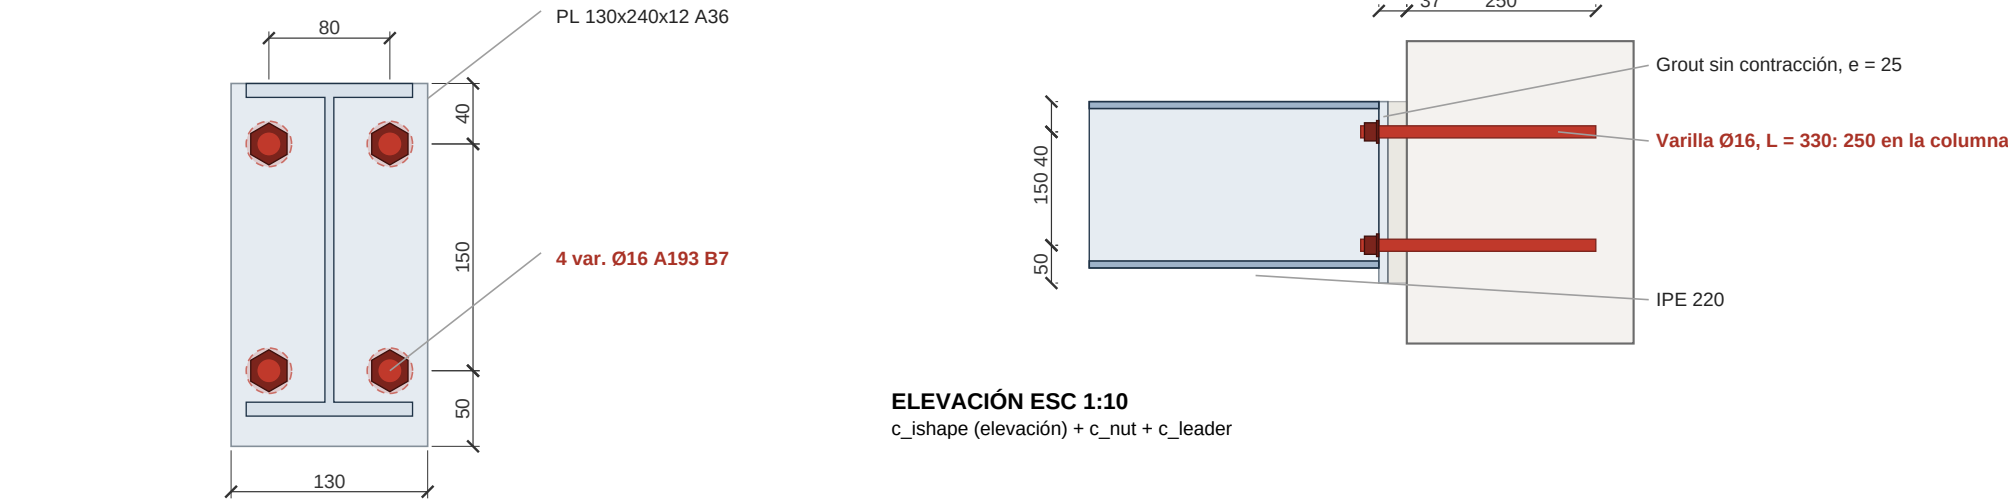


VISTA DE FRENTE ESC 1:5

c_plate + c_ishape + c_nut_front + c_leader

2. Secciones de hormigón

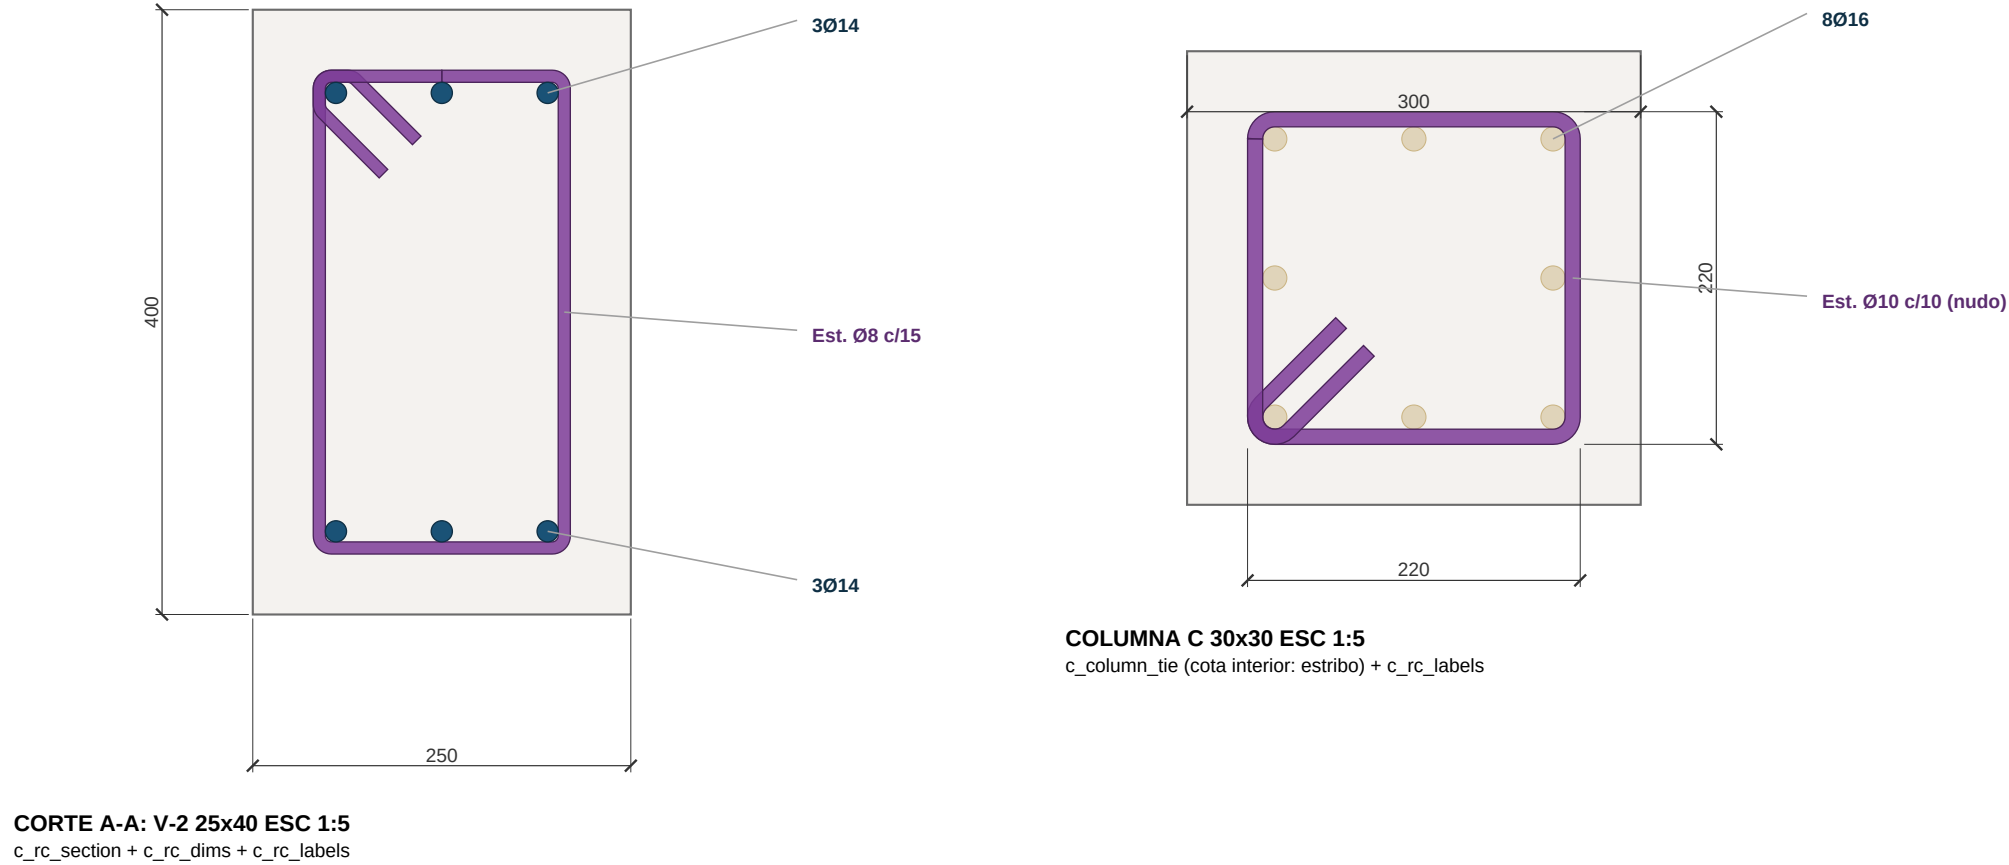

4. Piezas, cantidades y notas

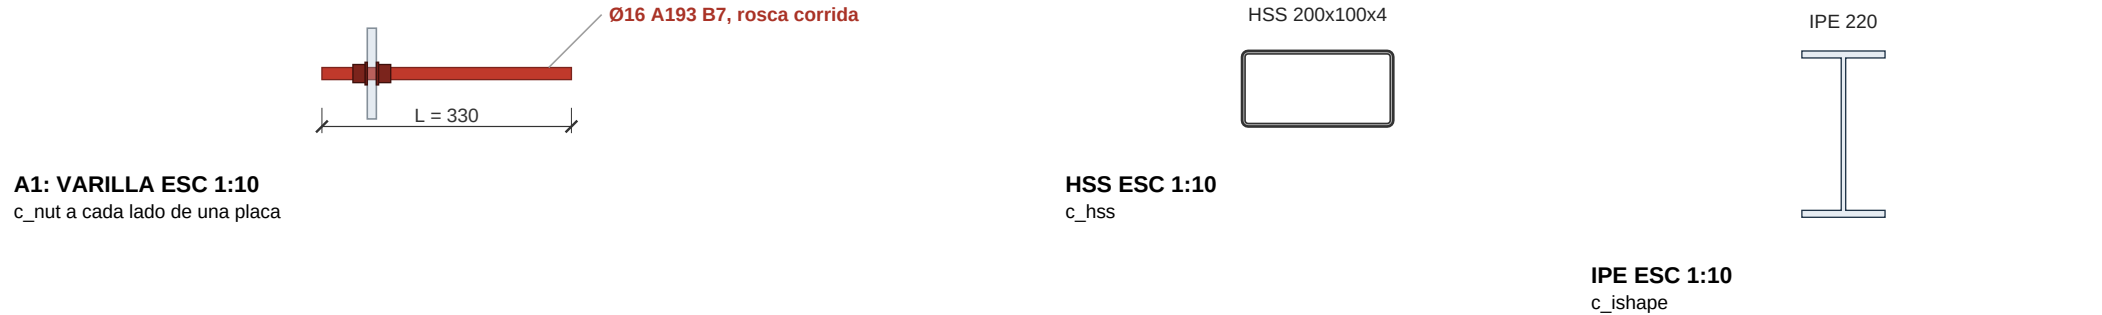

Cantidades (blk_table)

Marca	Elemento	Descripción	Cant.
A1	Varilla	Ø16 A193 B7, L = 330	4
P2	Placa extremo	PL 130x240x12 A36, 4 agujeros Ø18	1
T	Tuerca	Ø16 grado 8	4
BA	Barra extra	2Ø12, L = 3200	2

Notas (blk_note)

- Medidas en mm.
- Hormigón f_c 21 MPa; acero de refuerzo f_y 412 MPa.
- Supuestos: longitud de varilla y tuercas grado 8 no dados en el pedido.